

IDEJNI PROJEKAT STAMBENOG OBJEKTA

LOKACIJA : PLANINA GOLIJA

crtež:

nivo projekta:

IDR

Investitor: Ivan Milinković iz Čačka

Odgovorni projektant:
Žarko Petrović dipl.inž.arh.
broj licence 300M 99 214

razmera:

Layout ID
A.01.1

Revision



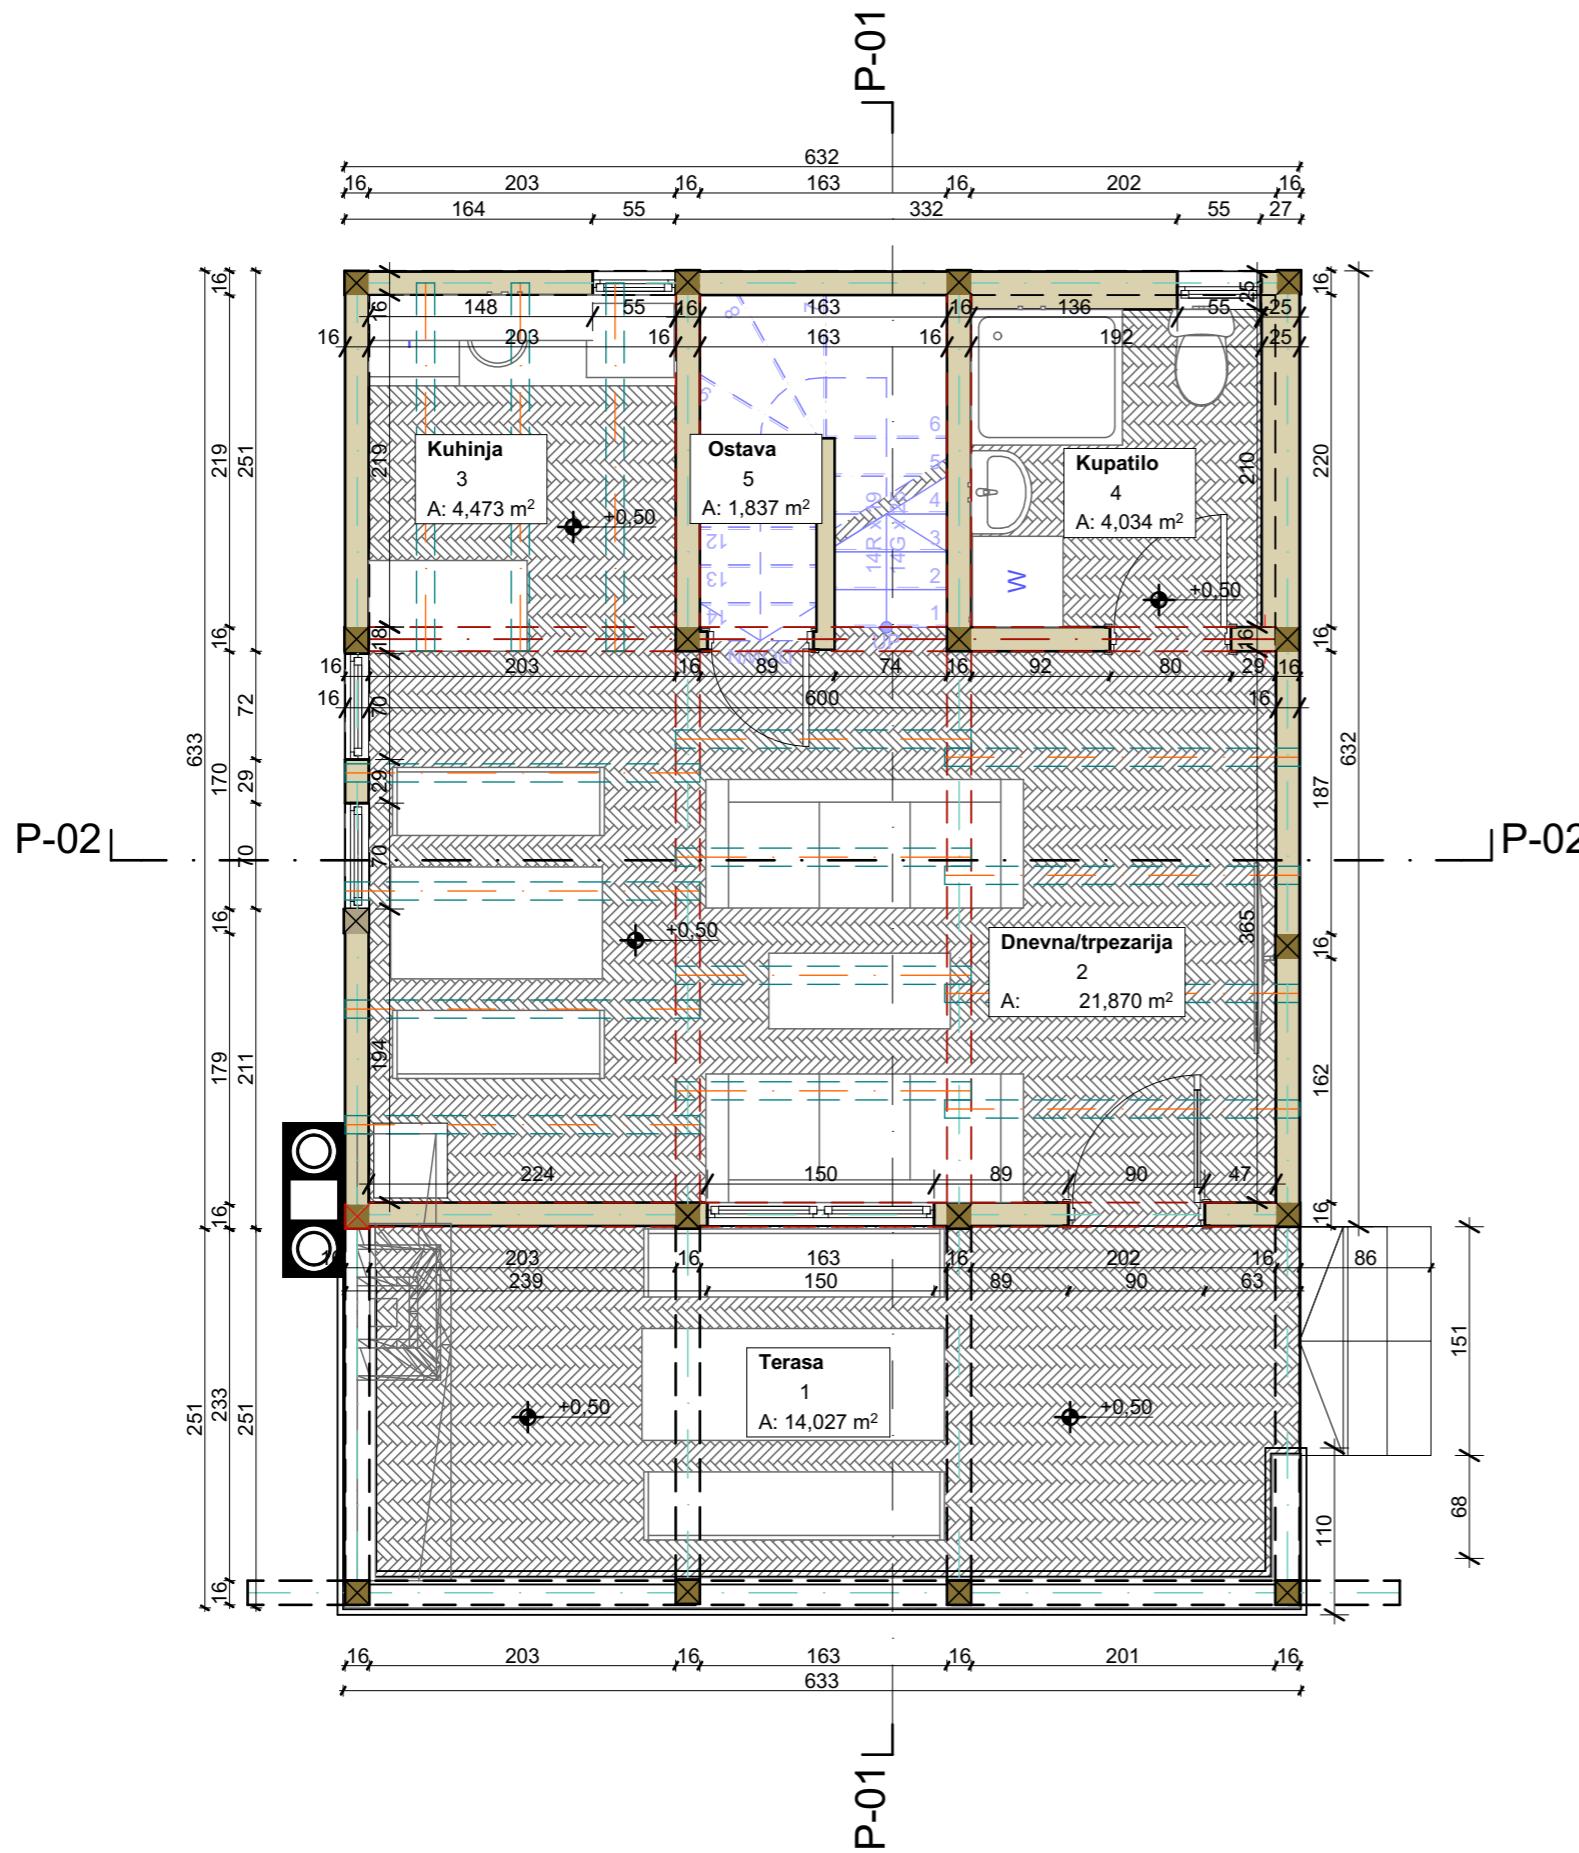


TABELA PROSTORIJE		
br.	naziv prostorije	Pov(m ²)
1.	Terasa	14,02
2.	Dnevna/trpezari	21,87
3.	Kuhinja	4,47
4.	Kupatilo	4,03
5.	Ostava	1,83
6.	Stepenište	3,86
7.	Hol	3,77
8.	WC	1,67
9.	Soba	6,12
10.	Soba	6,90
11.	Soba	6,94
12.	Garderoba	4,14
Pneto ukupno:79,62m²		

BRUTO POVRŠINA PRIZEMLJA
P: 55,960 m²

PBRUTO ukupno(BGRP):95,77m²

IDEJNI PROJEKAT STAMBENOG OBJEKTA	
LOKACIJA : PLANINA GOLIJA	
crtež:	
OSNOVA PRIZEMLJA	
nivo projekta:	
IDR	
Investitor: Ivan Milinković iz Čačka	
Odgovorni projektant: Žarko Petrović dipl.inž.arh. broj licence 300M 99 214	
razmera:	
1:50	
Layout ID	Revision
A.01.2	

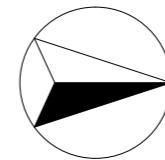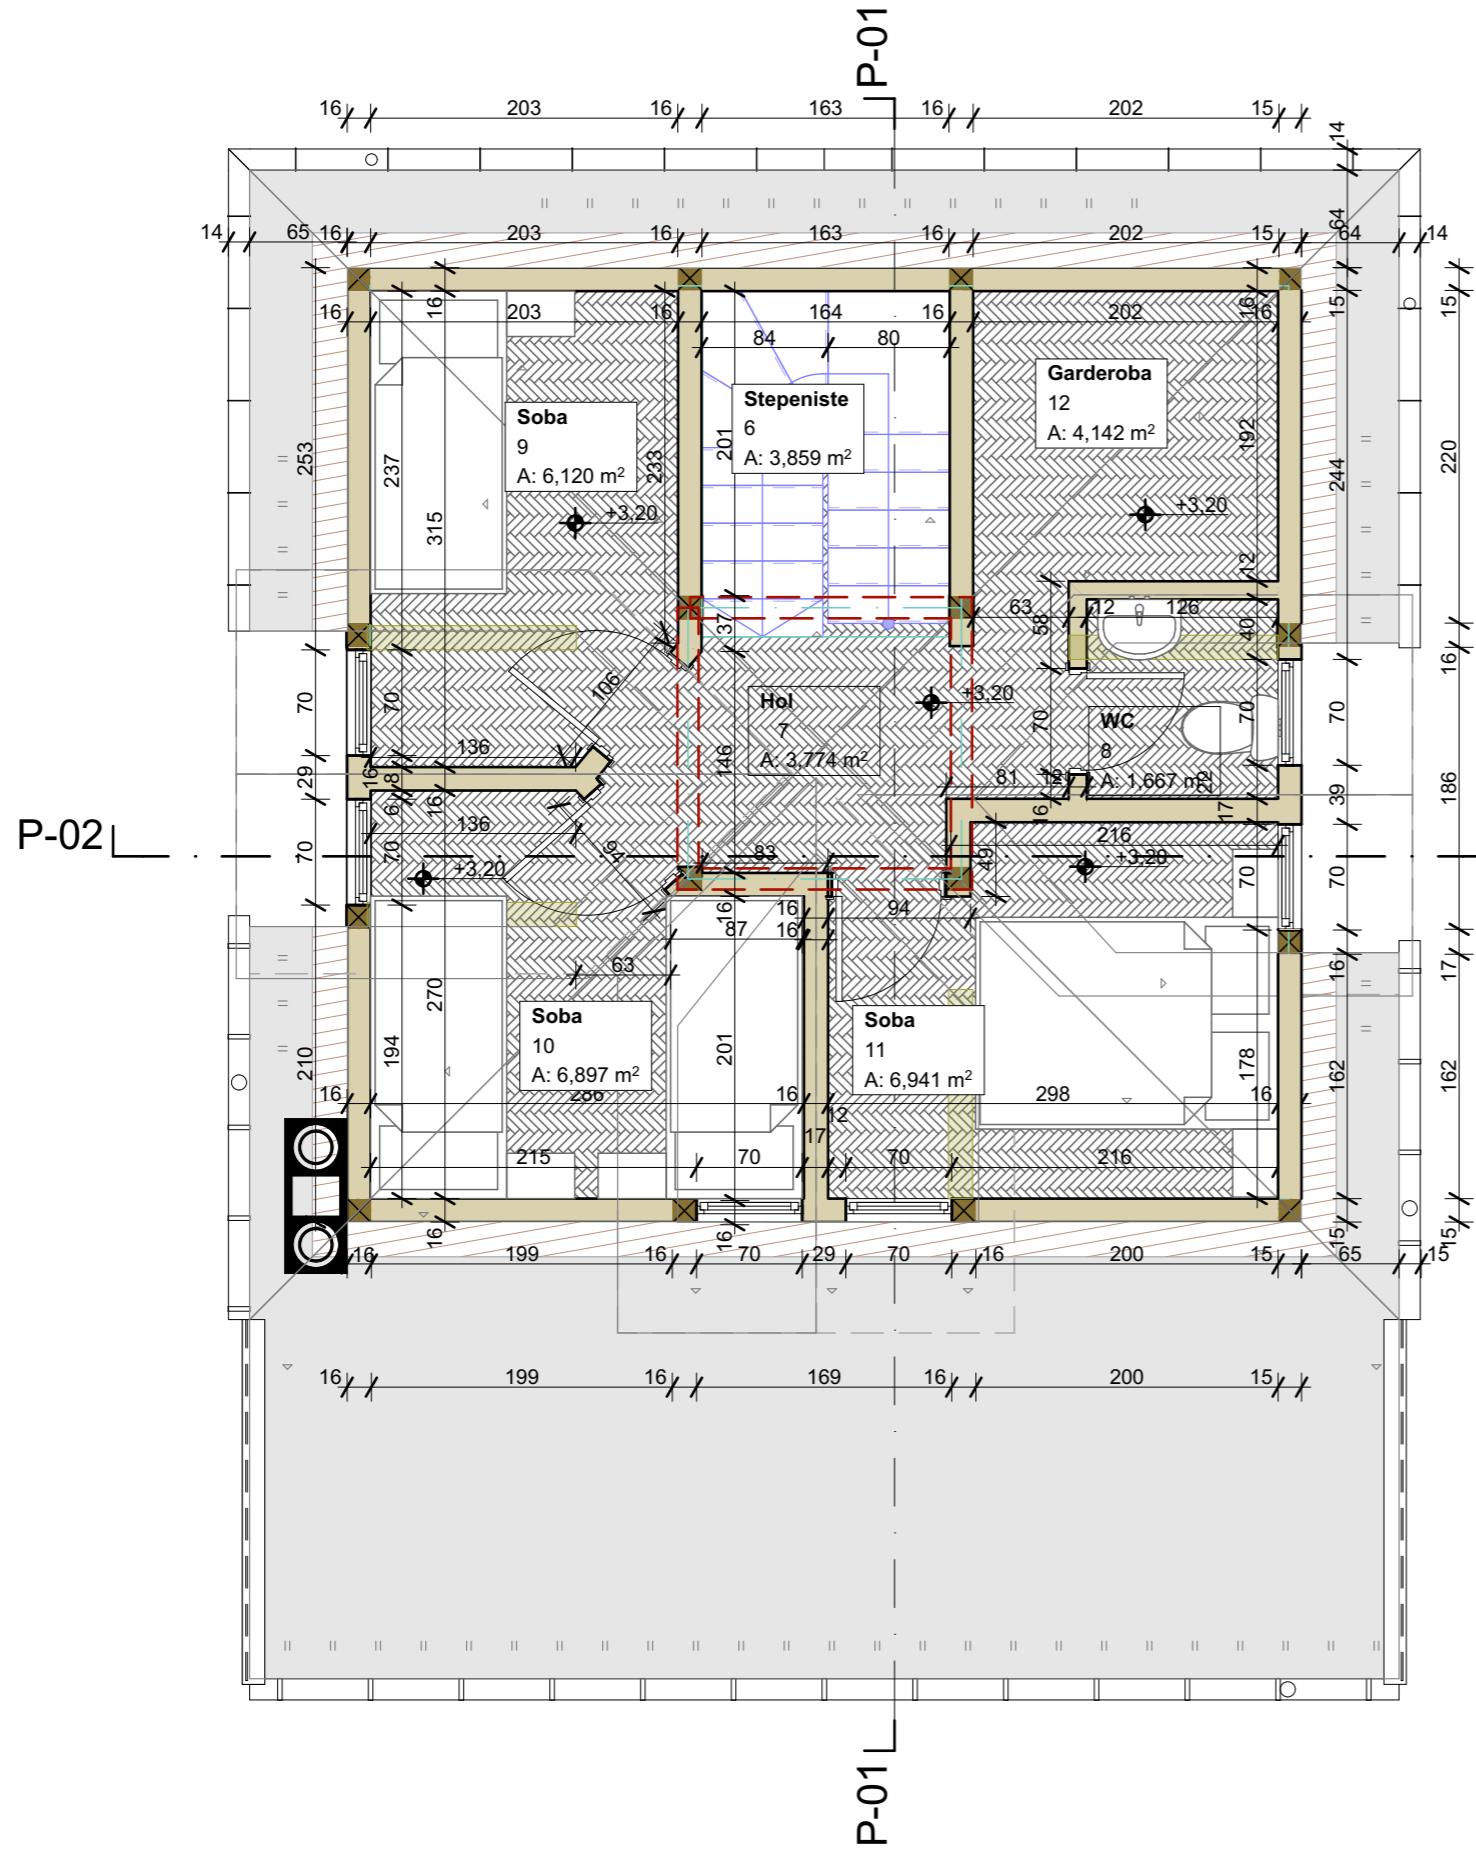

N

TABELA PROSTORIJE



br.	naziv prostorije	Pov(m ²)
1.	Terasa	14,02
2.	Dnevna/trpezari	21,87
3.	Kuhinja	4,47
4.	Kupatilo	4,03
5.	Ostava	1,83
6.	Stepenište	3,86
7.	Hol	3,77
8.	WC	1,67
9.	Soba	6,12
10.	Soba	6,90
11.	Soba	6,94
12.	Garderoba	4,14

Pneto ukupno: 79,62m²



BRUTO POVRŠINA POTKROVLJA
P: 39,816 m²

PBRUTO ukupno(BGRP):95,77m²

IDEJNI PROJEKAT STAMBENOG OBJEKTA
LOKACIJA : PLANINA GOLIJA
crtež:
OSNOVA POTKROVLJA
nivo projekta:
IDR
Investitor: Ivan Milinković iz Čačka
Odgovorni projektant: Žarko Petrović dipl.inž.arh. broj licence 300M 99 214
razmera:
1:50
Layout ID A.01.3
Revision

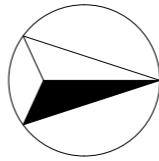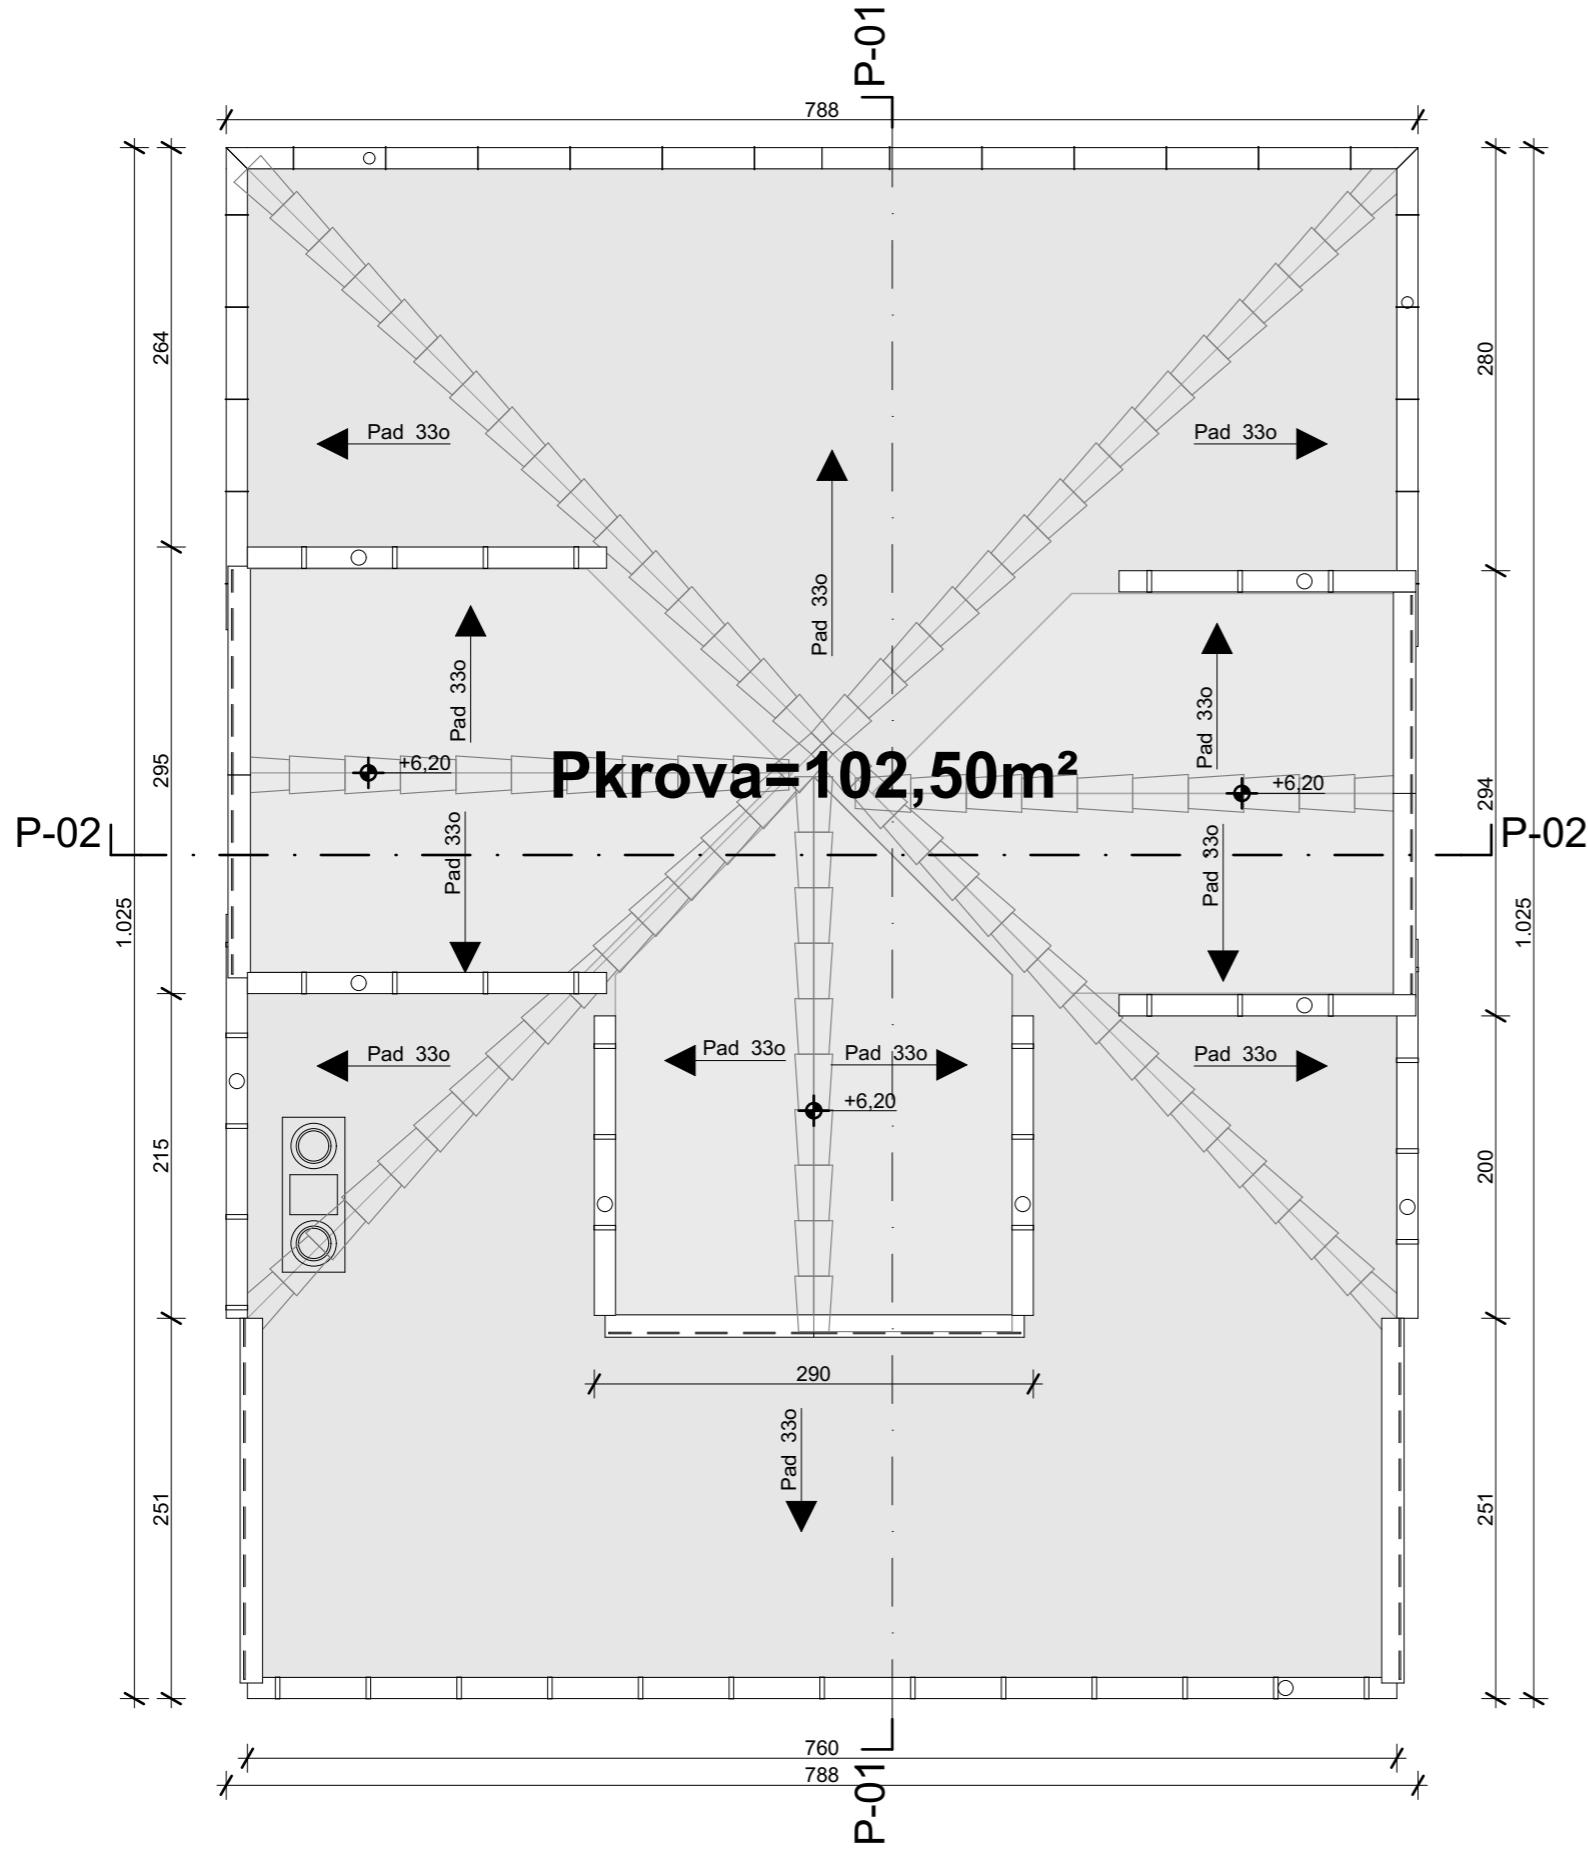

N

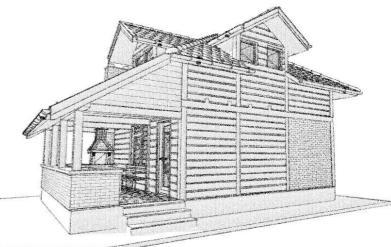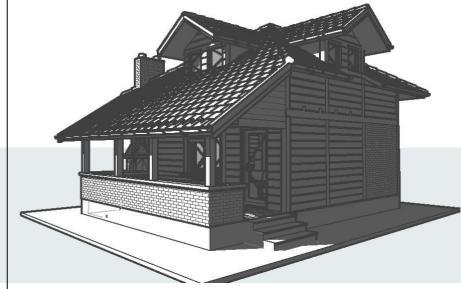

IDEJNI PROJEKAT STAMBENOG OBJEKTA

LOKACIJA : PLANINA GOLIJA

crtež:
Osnova krovnih ravni

nivo projekta:
IDR

Investitor: Ivan Milinković iz Čačka


Odgovorni projektant:
Žarko Petrović dipl.inž.arh.
broj licence 300M 99 214

razmera:




1:50

Layout ID
A.01.4

Revision

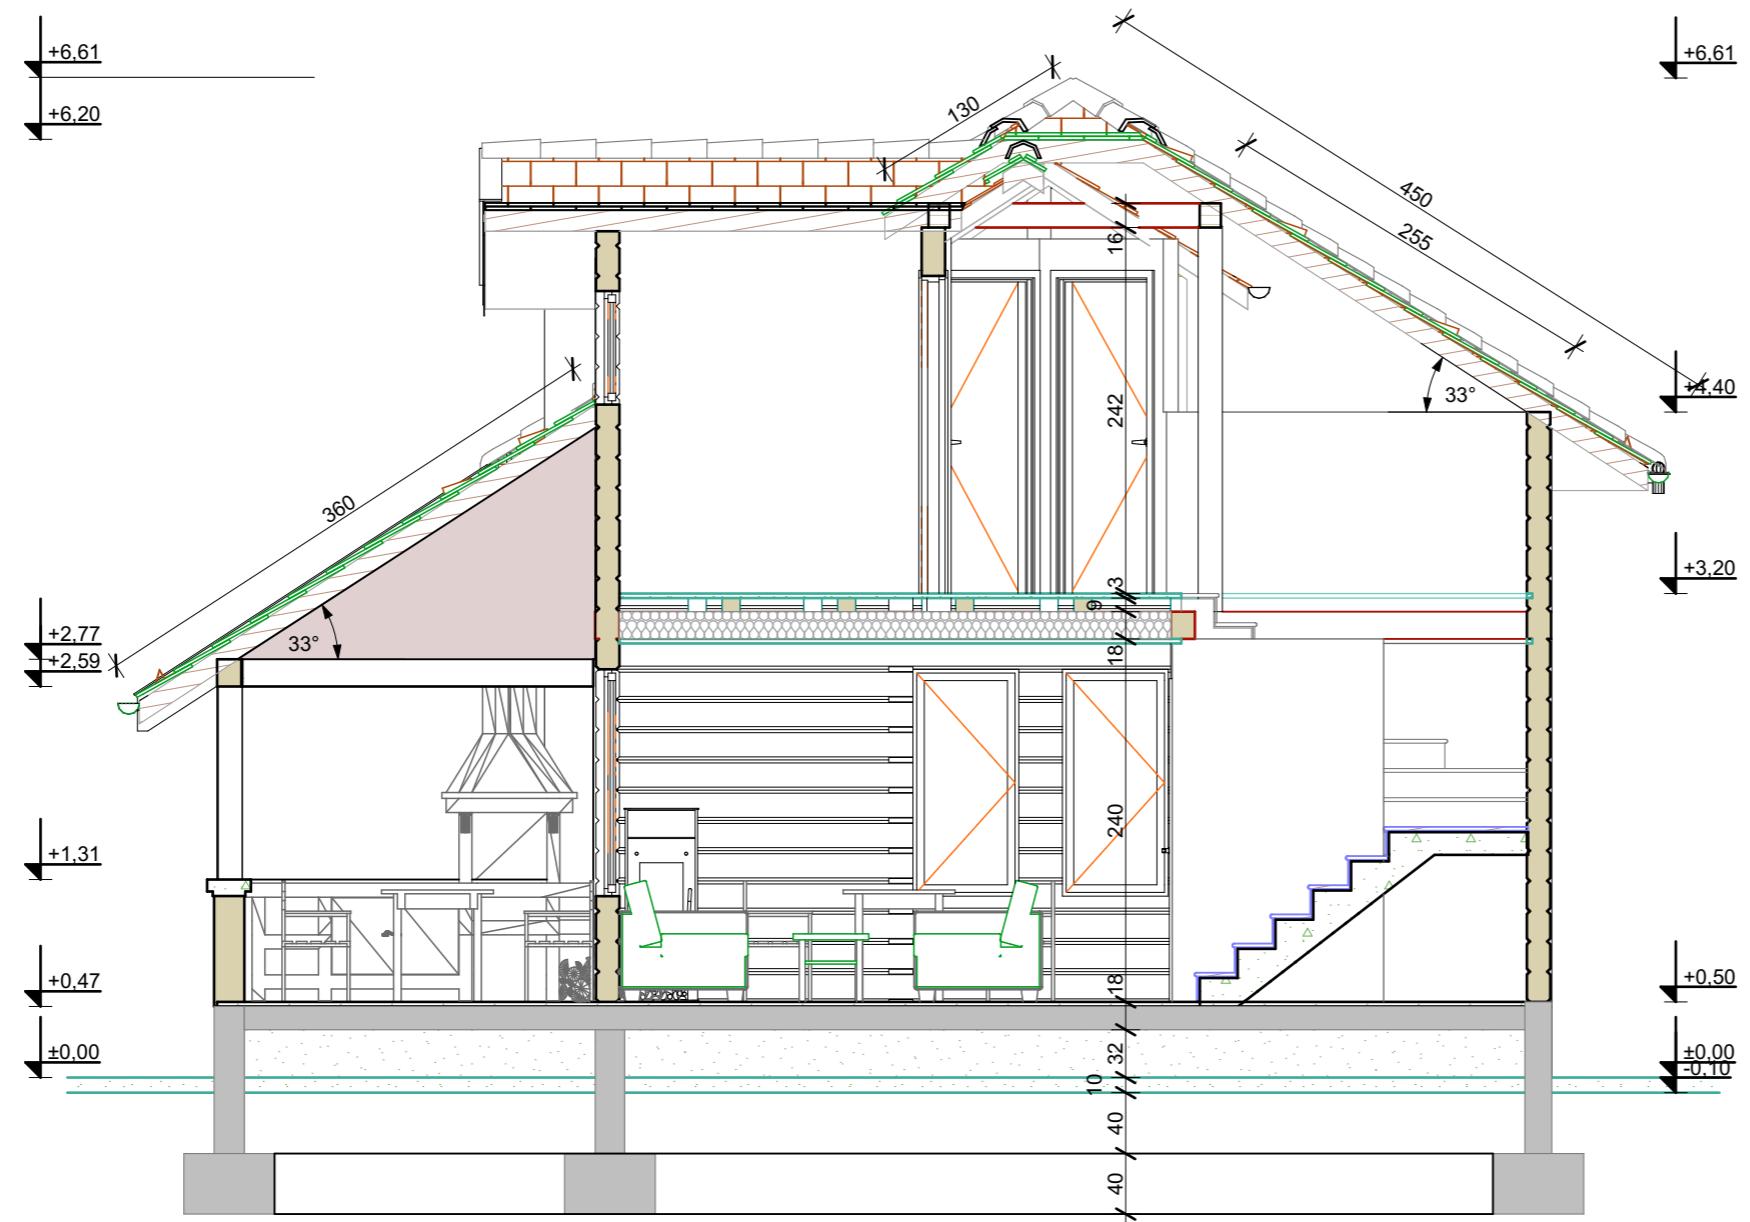

IDEJNI PROJEKAT STAMBENOG OBJEKTA	
LOKACIJA : PLANINA GOLIJA	
crtež:	
PRESEK	
nivo projekta:	
IDR	
Investitor: Ivan Milinković iz Čačka	
Odgovorni projektant: Žarko Petrović dipl.inž.arh. broj licence 300M 99 214	
razmera:	
1:50	
Layout ID	Revision
A.02	

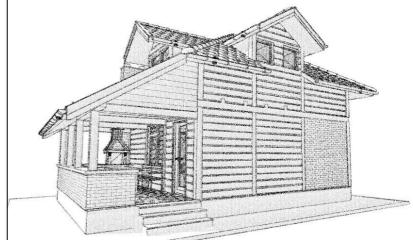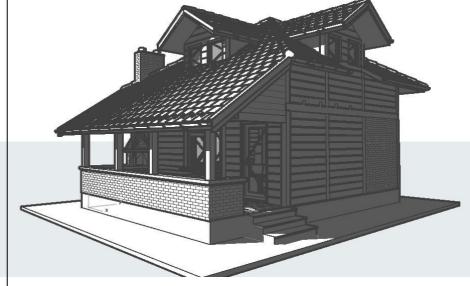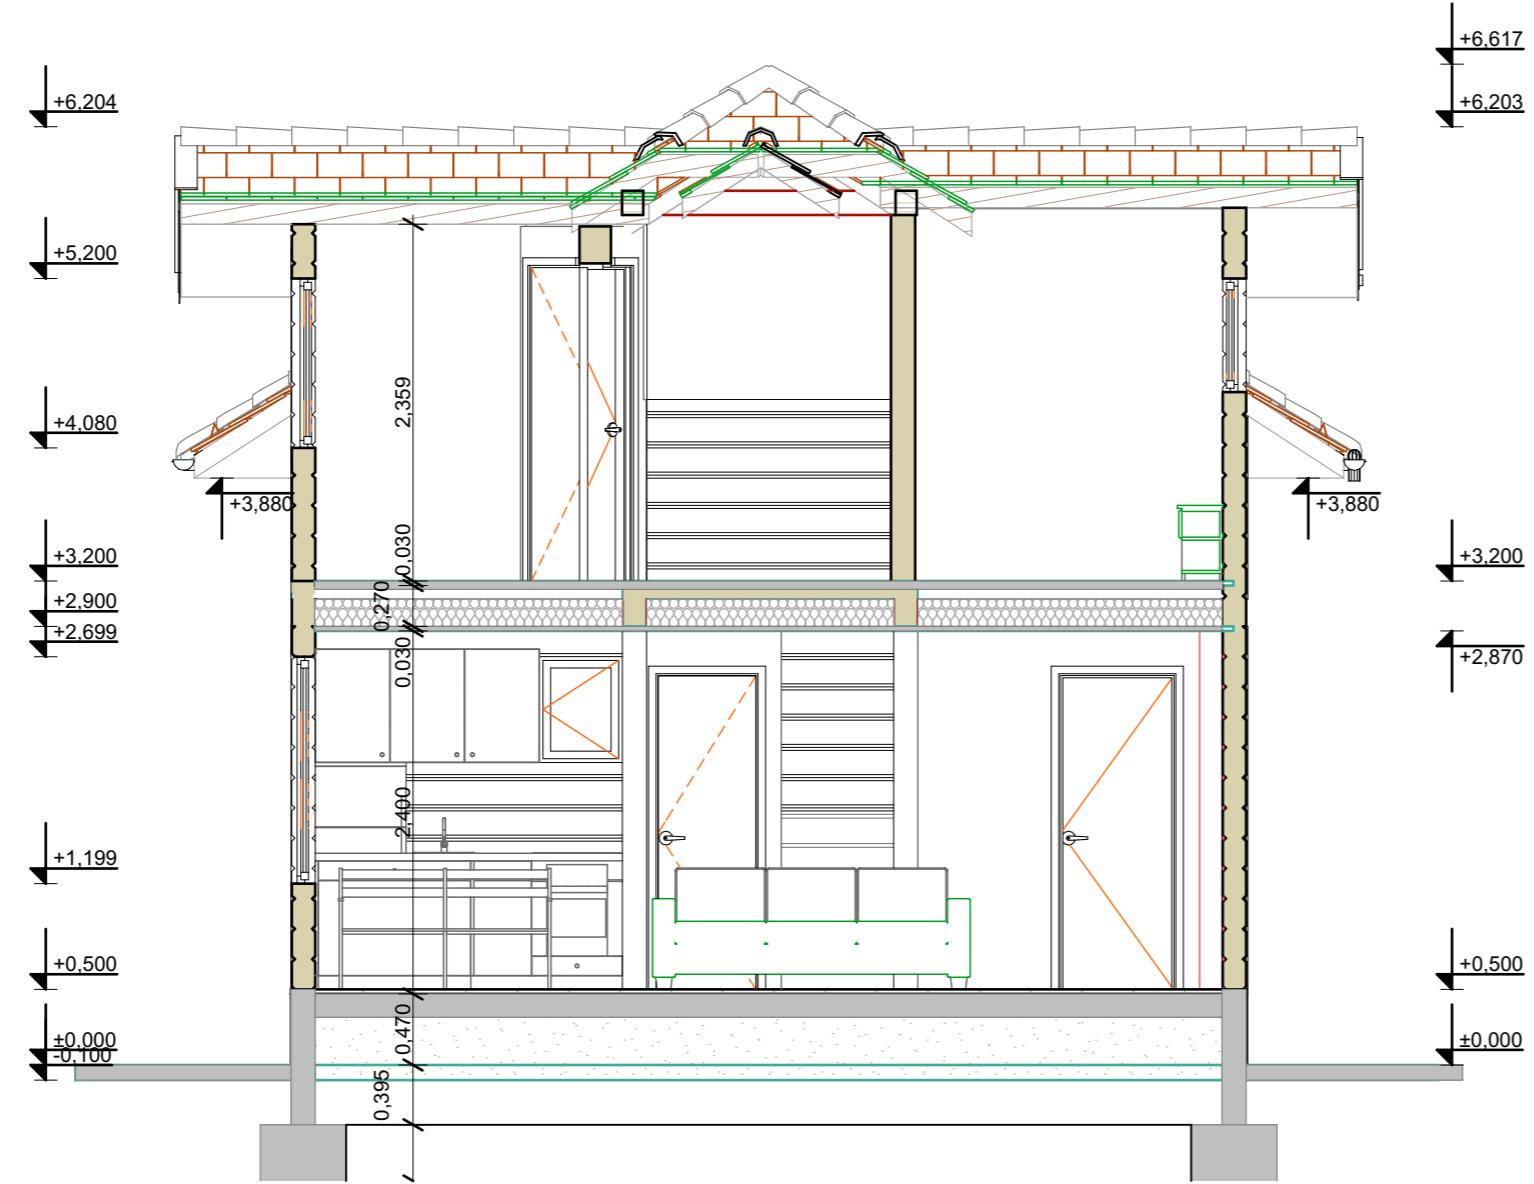

IDEJNI PROJEKAT STAMBENOG OBJEKTA

LOKACIJA : PLANINA GOLIJA

crtež:

PRESEK

nivo projekta:

IDR

Investitor: Ivan Milinković iz Čačka

Odgovorni projektant:
Žarko Petrović dipl.inž.arh.
broj licence 300M 99 214




razmara:

1:50

Layout ID

A.03

Revision

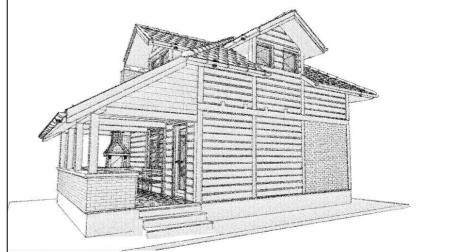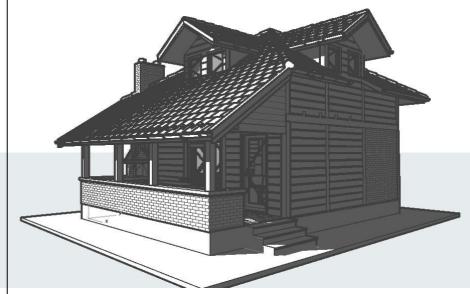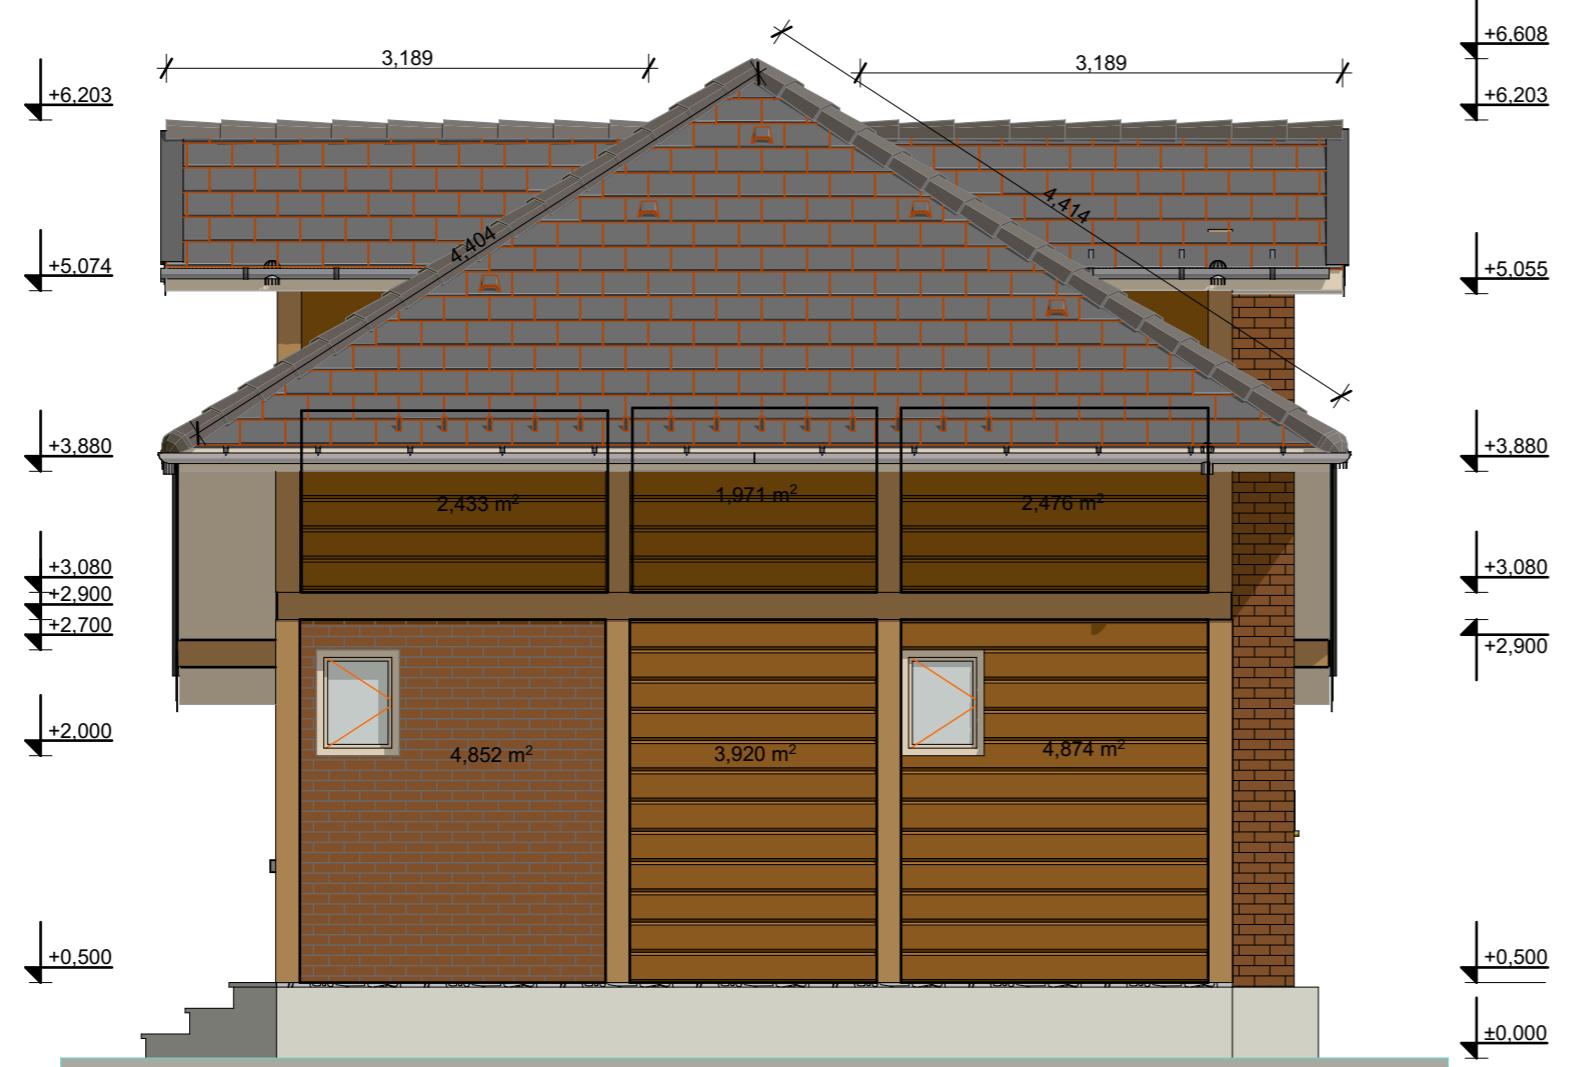

IDEJNI PROJEKAT STAMBENOG OBJEKTA

LOKACIJA : PLANINA GOLIJA

crtež:

ZAPADNA FASADA

nivo projekta:

IDR

Investitor: Ivan Milinković iz Čačka

Odgovorni projektant:
Žarko Petrović dipl.inž.arh.
broj licence 300M 99 214




razmera:

1:50

Layout ID

A.04.1

Revision

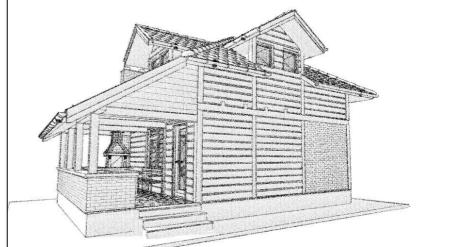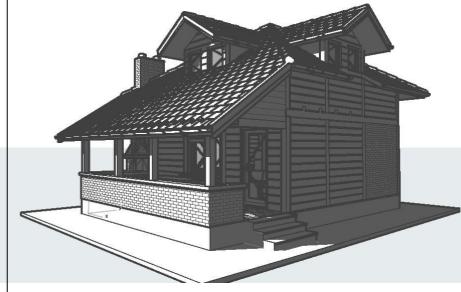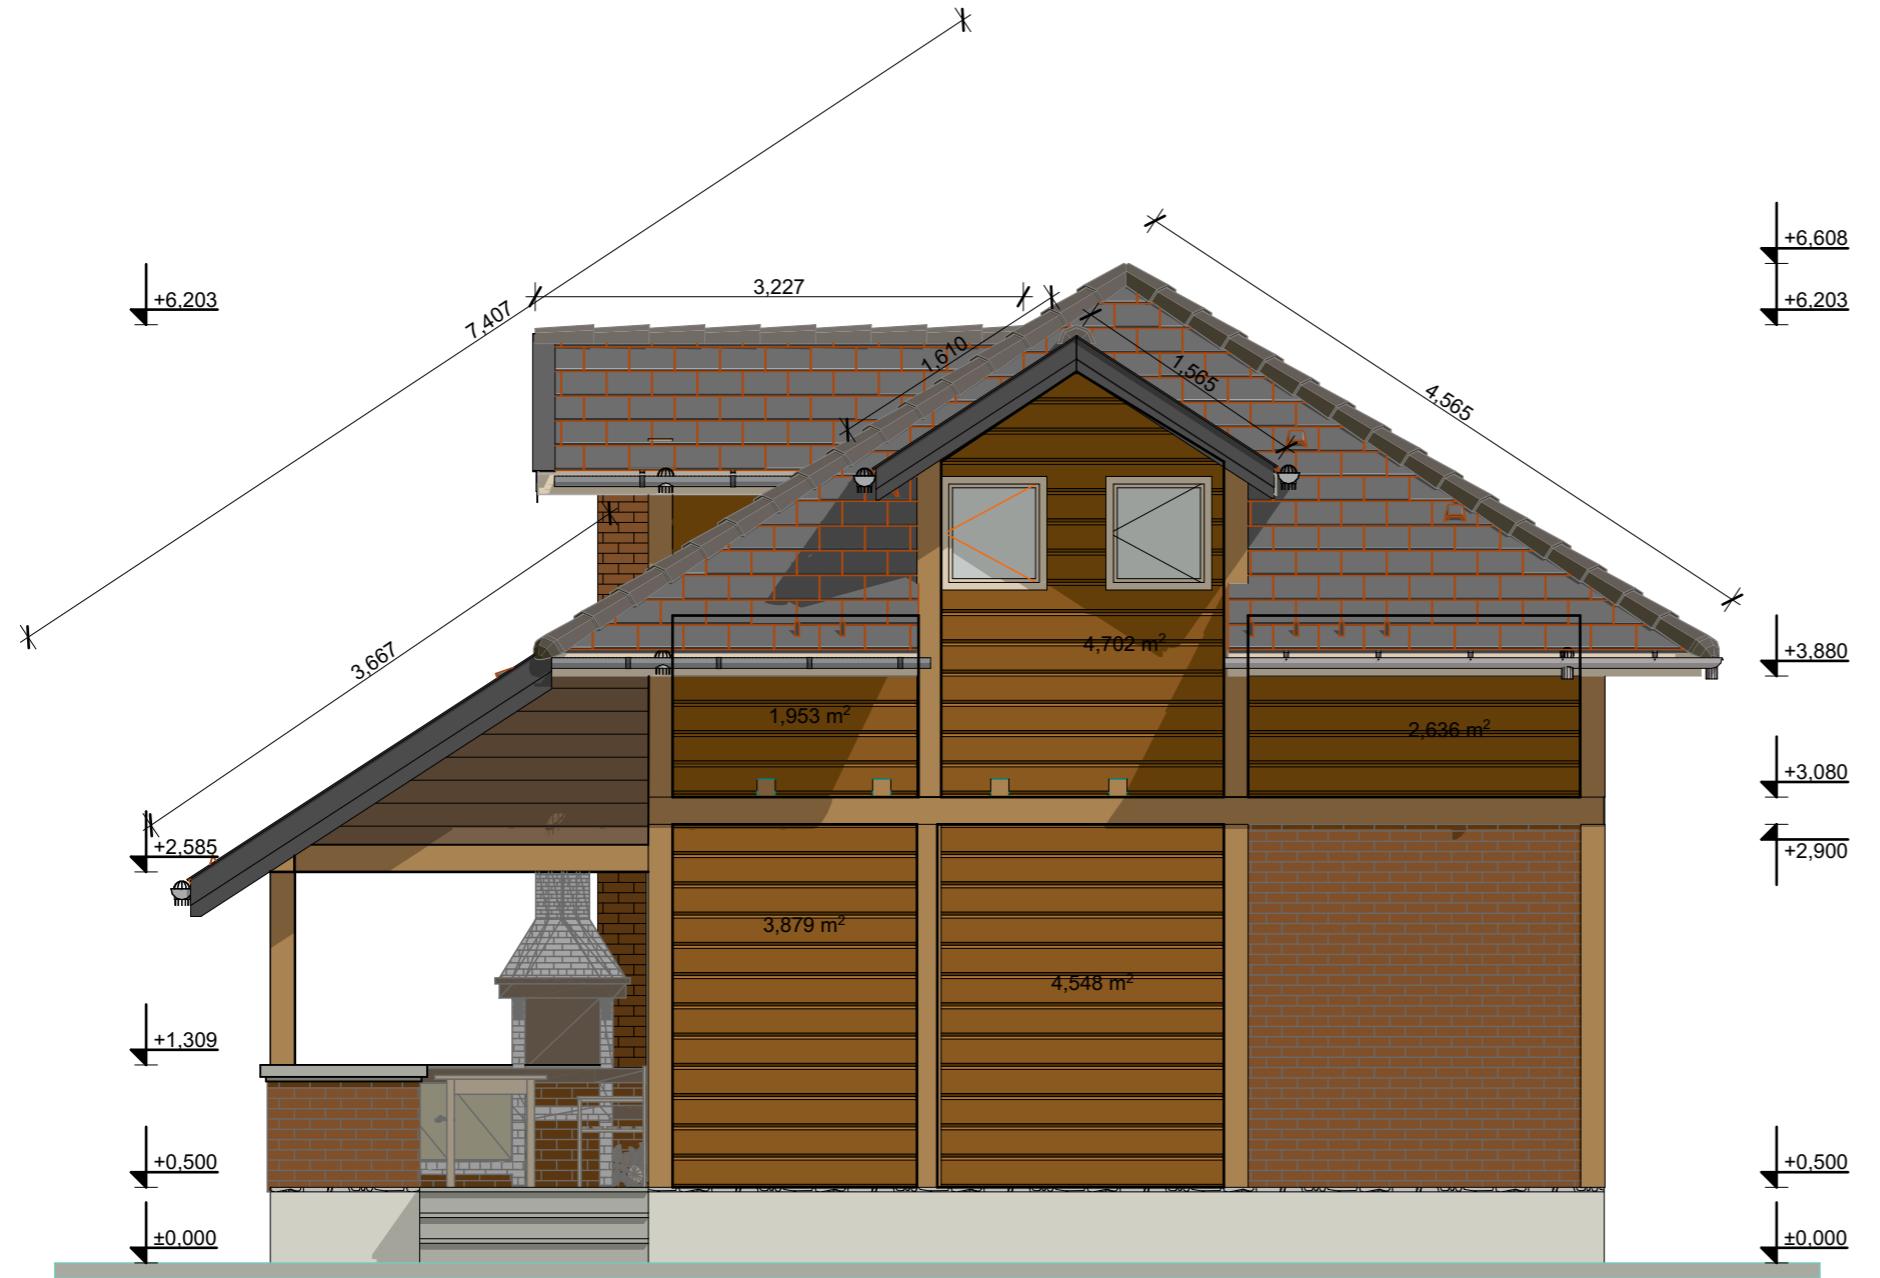

IDEJNI PROJEKAT STAMBENOG OBJEKTA

LOKACIJA : PLANINA GOLIJA

crtež:
SEVERNA FASADA


nivo projekta:
IDR

Investitor: Ivan Milinković iz Čačka

Odgovorni projektant:
Žarko Petrović dipl.inž.arh.
broj licence 300M 99 214

razmera:
1:50

Layout ID **A.04.2** Revision

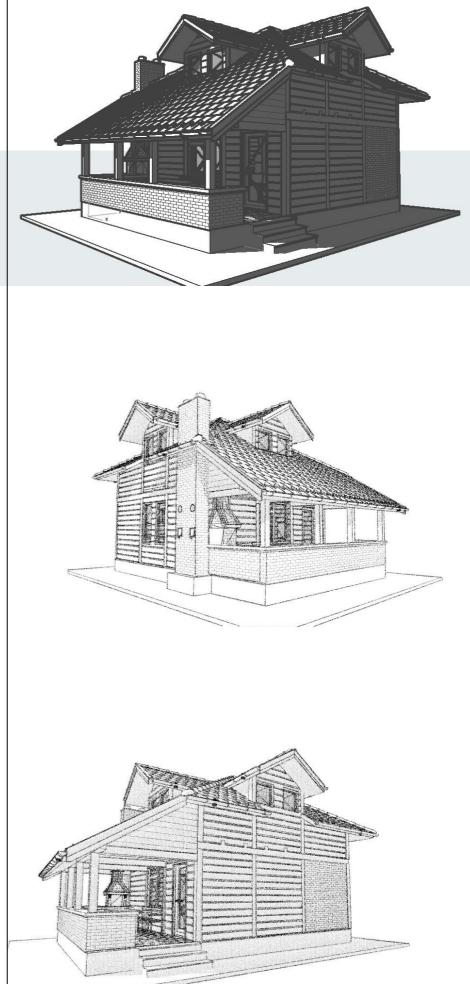

IDEJNI PROJEKAT STAMBENOG OBJEKTA

LOKACIJA : PLANINA GOLIJA

crtež:
ISTOČNA FASADA


nivo projekta:
IDR

Investitor: Ivan Milinković iz Čačka

Odgovorni projektant:
Žarko Petrović dipl.inž.arh.
broj licence 300M 99 214

razmera:
1:50

Layout ID **A.04.3** Revision

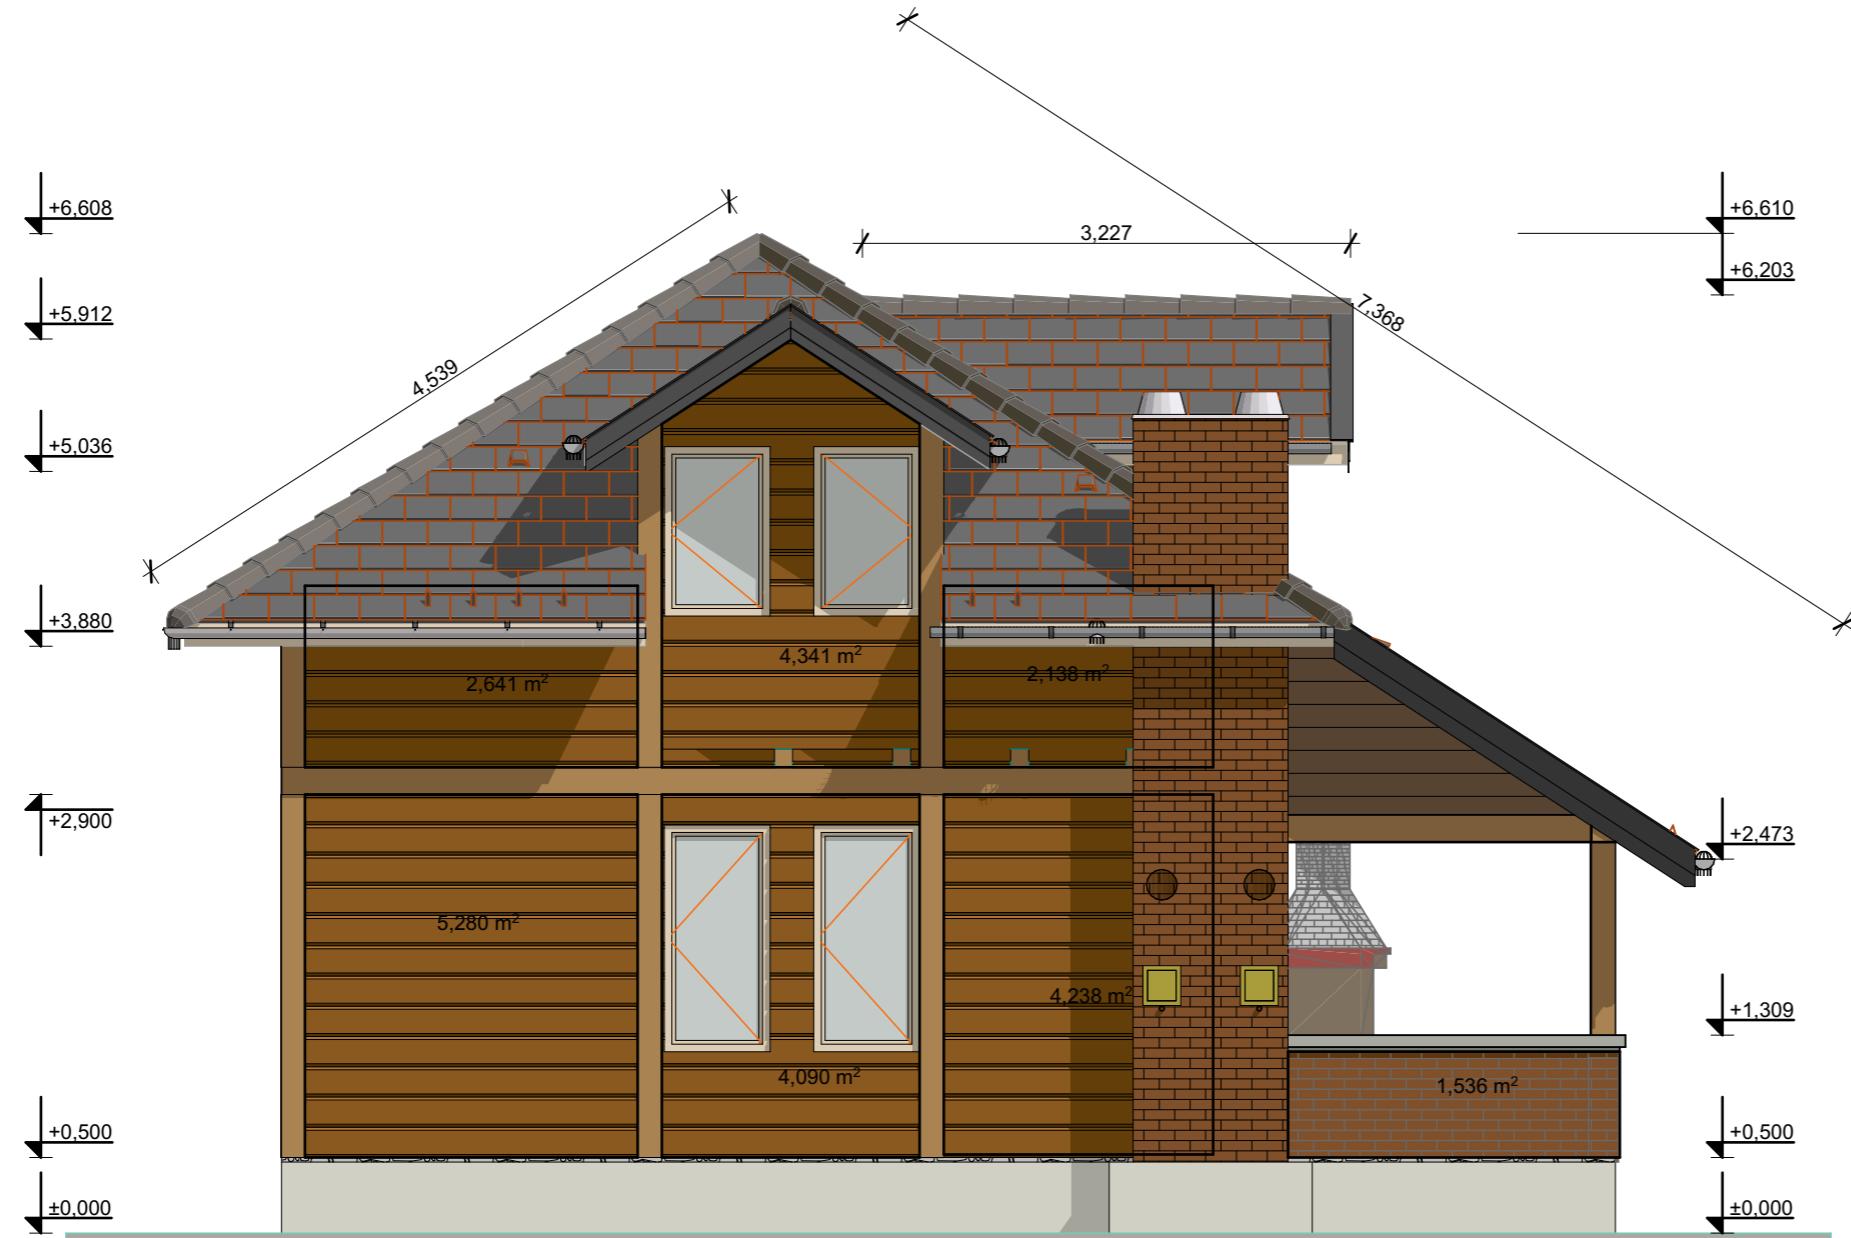

IDEJNI PROJEKAT STAMBENOG OBJEKTA

LOKACIJA : PLANINA GOLIJA

crtež:
JUŽNA FASADA

nivo projekta:
IDR

Investitor: Ivan Milinković iz Čačka

Odgovorni projektant:
Žarko Petrović dipl.inž.arh.
broj licence 300M 99 214

razmera:
1:50

Layout ID **A.04.4** Revision